


BESTEK


**RUMAH TOKO
BABY SPA
2 LANTAI**

JL. TENTARA PELAJAR, GIRIWONO, WONOGIRI

TAHUN 2024

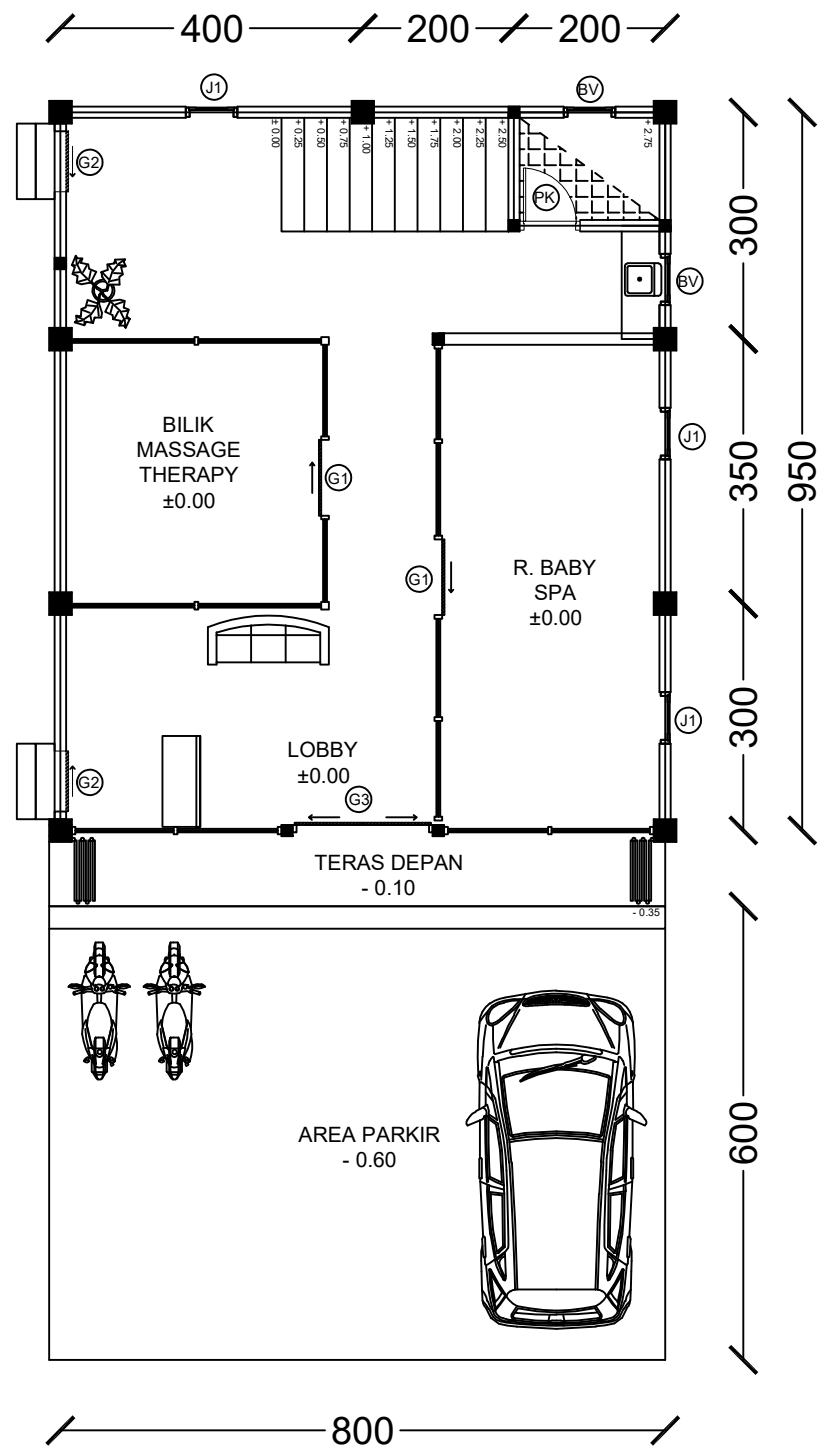


DENAH LANTAI 1
SKALA 1 : 100

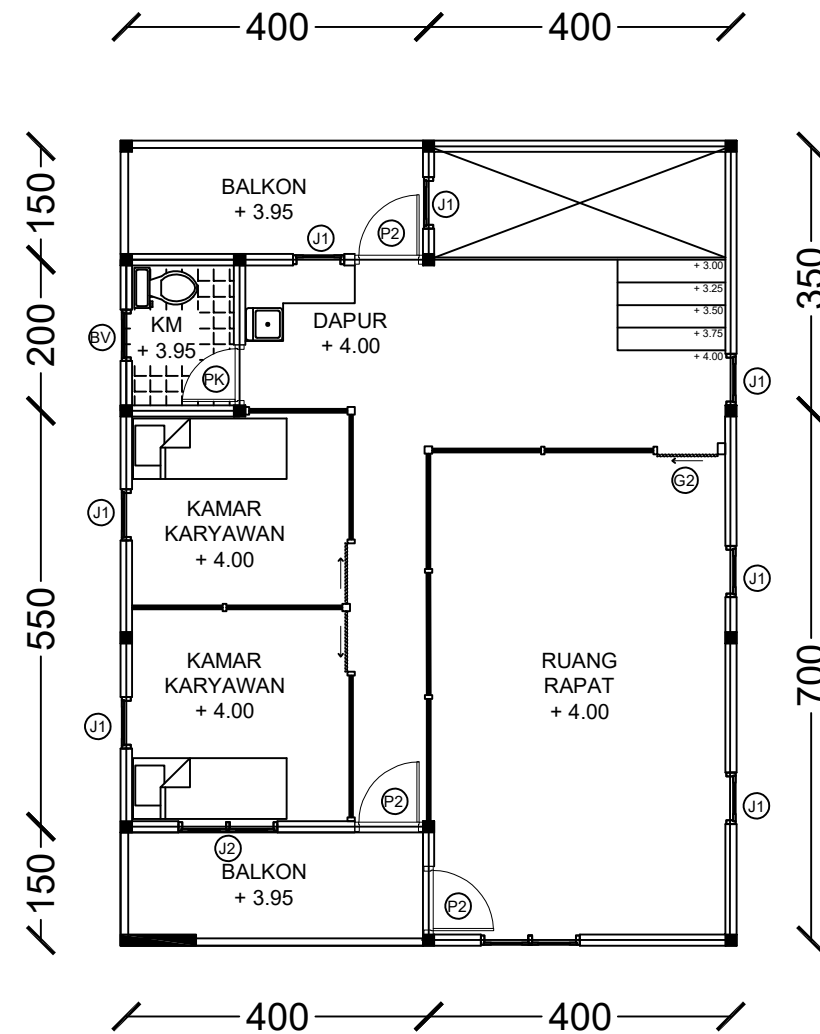


DENAH LANTAI 2
SKALA 1 : 100

NAMA PROYEK	
PEMBANGUNAN RUKO KLINIK BERSALIN & BABY SPA 2 LANTAI	
ALAMAT PROYEK	
JL. TENTARA PELAJAR, GIRIWONO, WONOGIRI	
GAMBAR	SKALA
DENAH LANTAI 1	1 : 100
DIGAMBAR	
BAGGUS PRASTYO S.T	
DIPERIKSA	DISETUJUI
HALAMAN	JML. HALAMAN

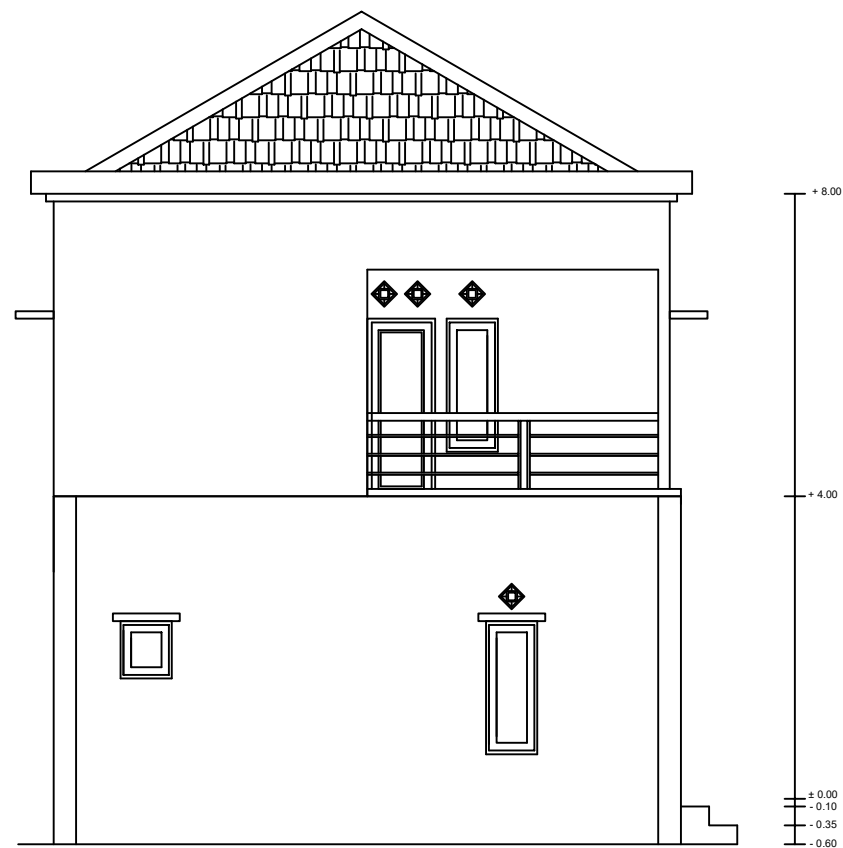

 **TAMPAK BELAKANG**
SKALA 1 : 100

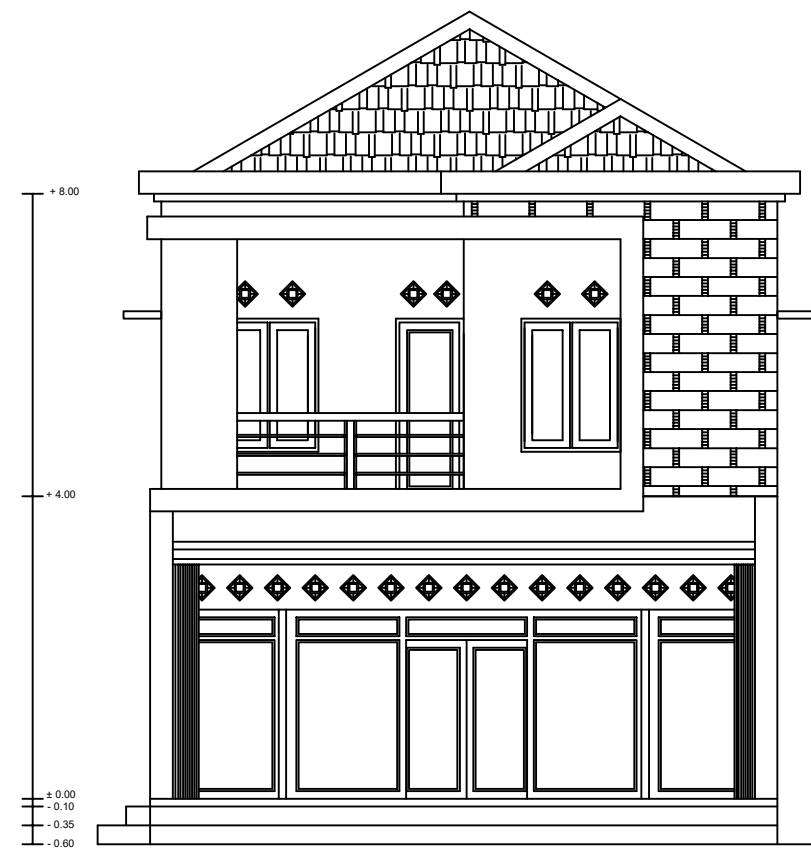

 **TAMPAK DEPAN**
SKALA 1 : 100

NAMA PROYEK

PEMBANGUNAN RUKO
KLINIK BERSALIN & BABY SPA
2 LANTAI

ALAMAT PROYEK

JL. TENTARA PELAJAR, GIRIWONO,
WONOGIRI

GAMBAR

SKALA

TAMPAK DEPAN &
BELAKANG

1 : 100

DIGAMBAR


BAGGUS PRASTYO S.T

DIPERIKSA


DISETUJUI

HALAMAN

JML. HALAMAN

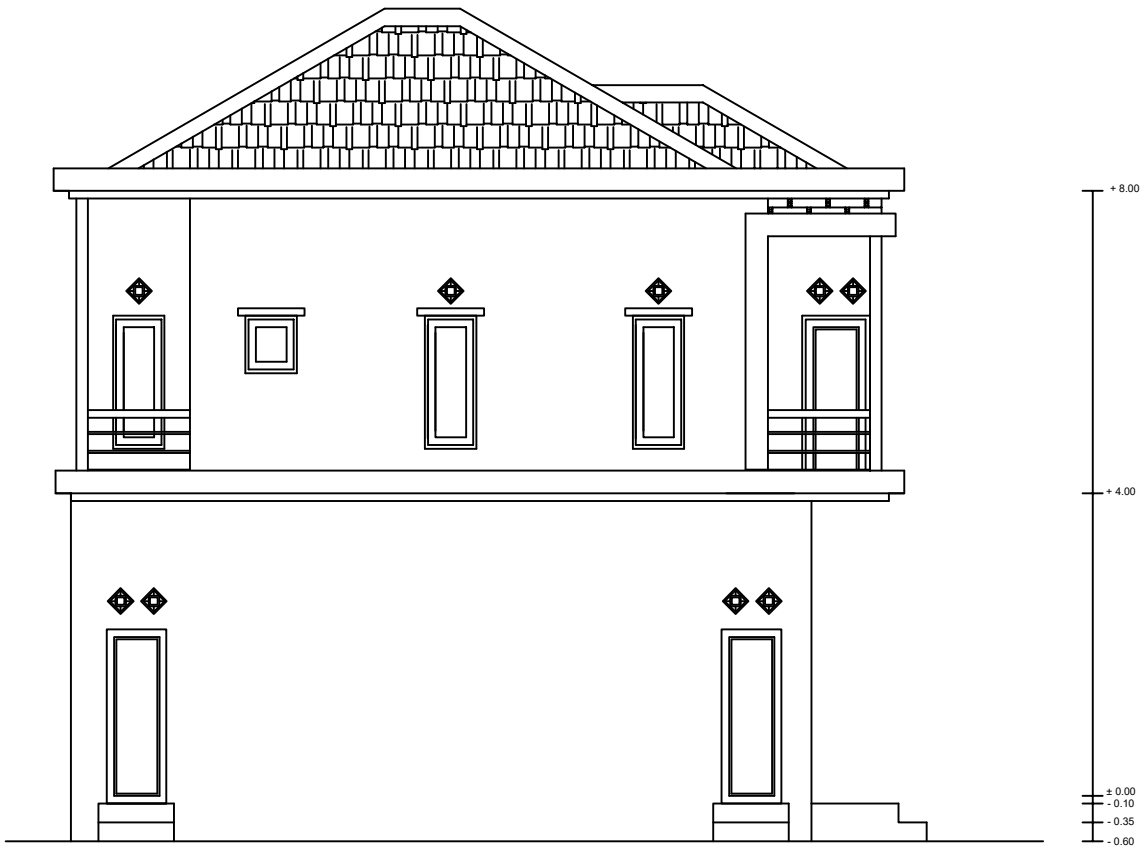


SAMPING KANAN
SKALA 1 : 100

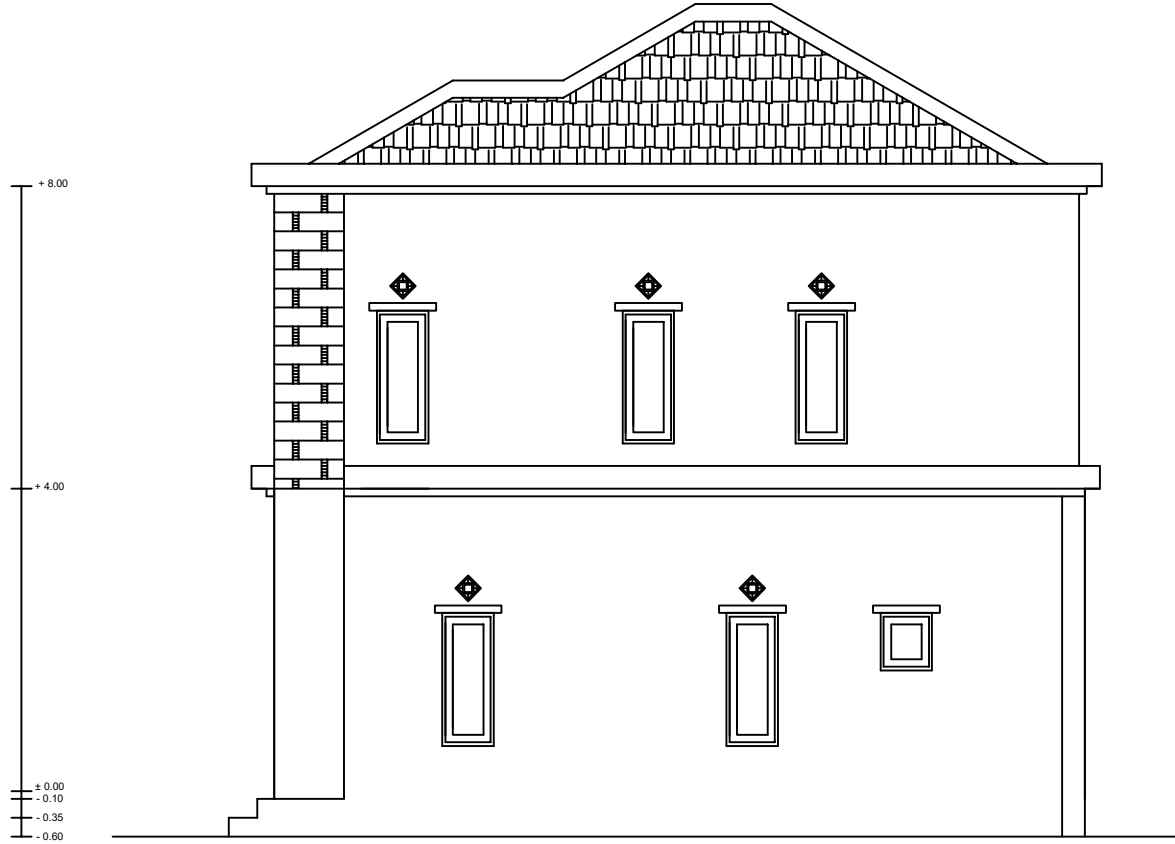


SAMPING KIRI
SKALA 1 : 100


NAMA PROYEK	
PEMBANGUNAN RUKO KLINIK BERSALIN & BABY SPA 2 LANTAI	
ALAMAT PROYEK	
JL. TENTARA PELAJAR, GIRIWONO, WONOGIRI	
GAMBAR	SKALA
TAMPAK SAMPING	1 : 100
DIGAMBAR	
BAGGUS PRASTYO S.T	
DIPERIKSA	DISETUJUI
HALAMAN	JML. HALAMAN

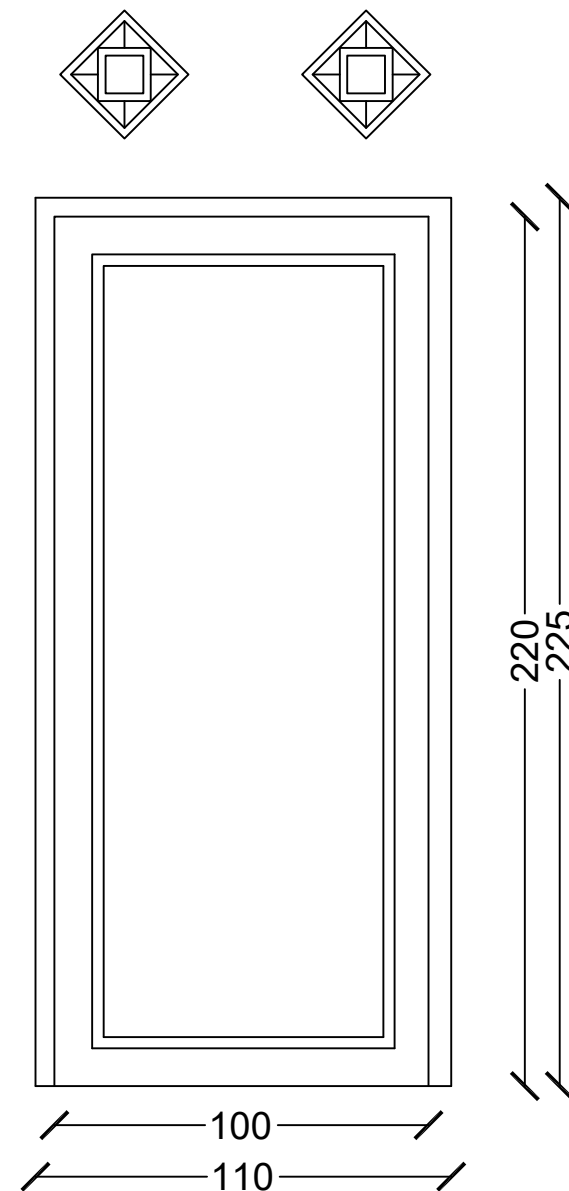

DETAIL P1
SKALA 1 : 20

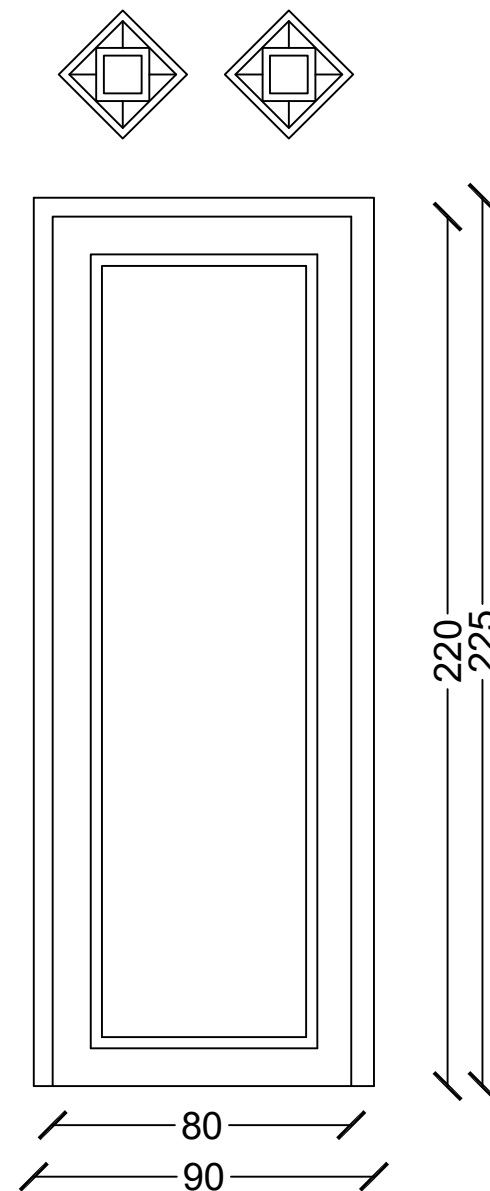


DETAIL P2
SKALA 1 : 20

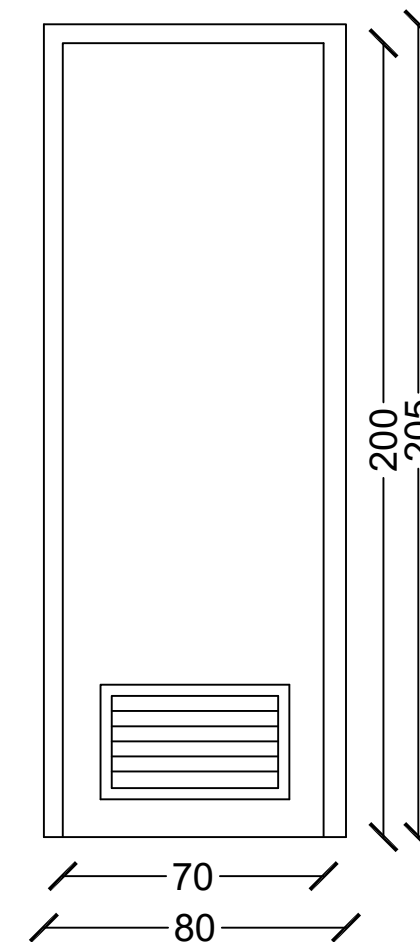


DETAIL PK
SKALA 1 : 20


NAMA PROYEK	
PEMBANGUNAN RUKO KLINIK BERSALIN & BABY SPA 2 LANTAI	
ALAMAT PROYEK	
JL. TENTARA PELAJAR, GIRIWONO, WONOGIRI	
GAMBAR	SKALA
DETAIL PINTU	1 : 100
DIGAMBAR	
BAGGUS PRASTYO S.T	
DIPERIKSA	DISETUJUI
HALAMAN	JML. HALAMAN

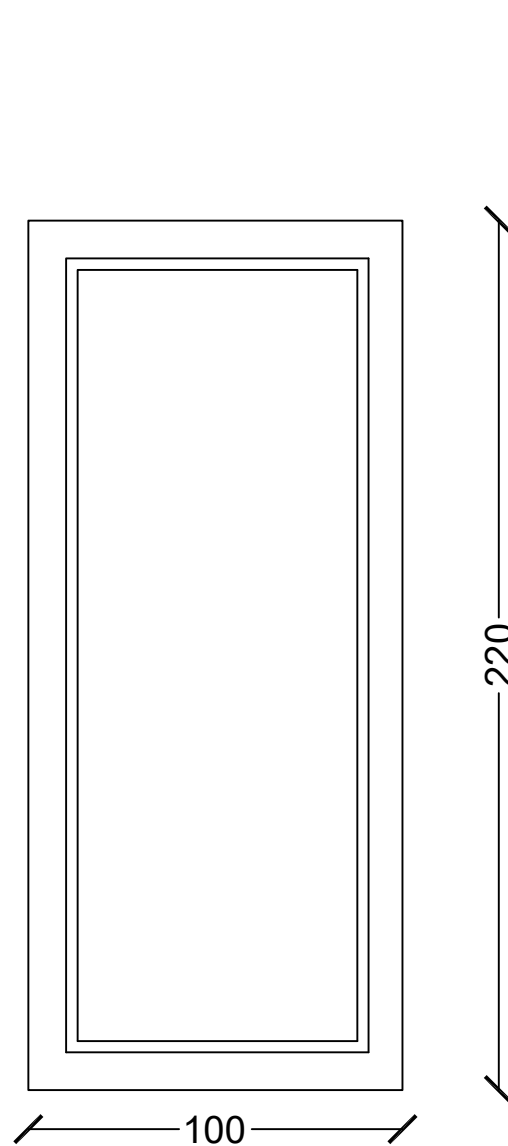

 **DETAIL G1**
SKALA 1 : 20

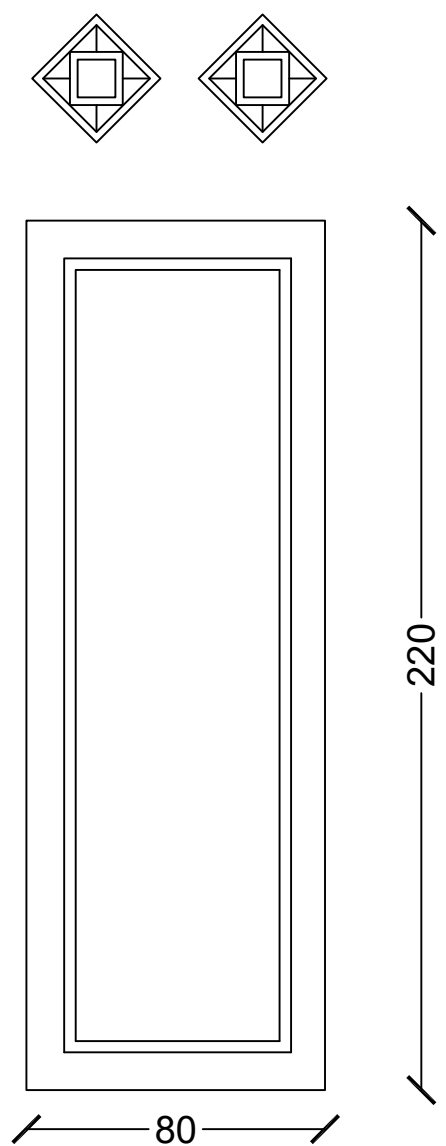


 **DETAIL G2**
SKALA 1 : 20

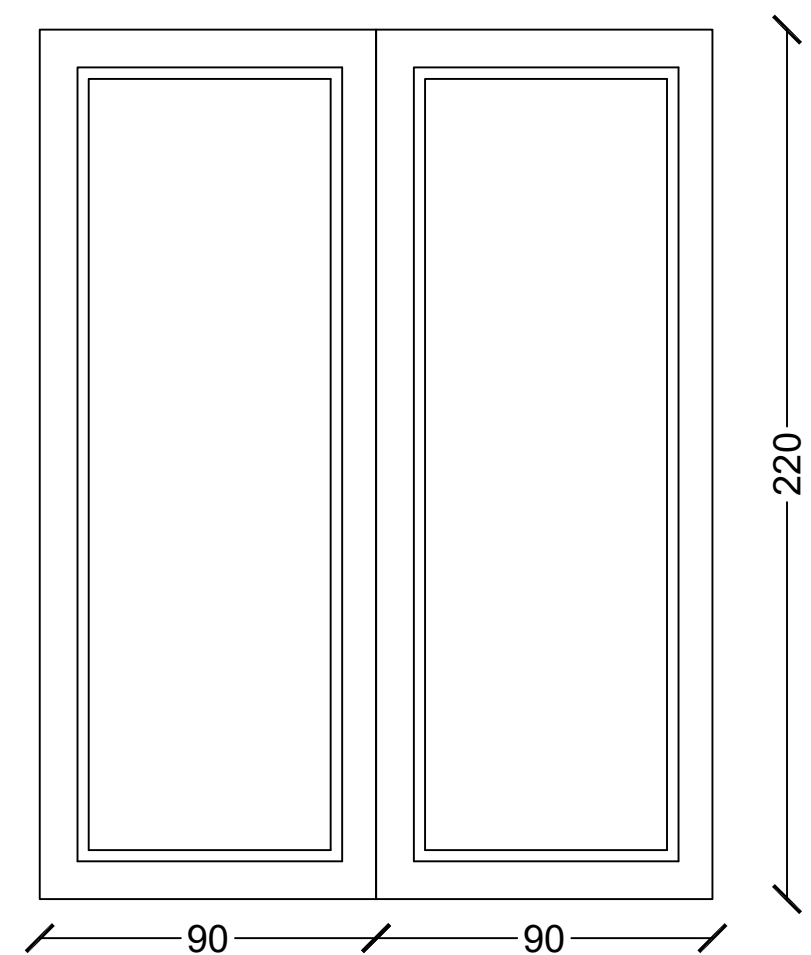


 **DETAIL G3**
SKALA 1 : 20


NAMA PROYEK	
PEMBANGUNAN RUKO KLINIK BERSALIN & BABY SPA 2 LANTAI	
ALAMAT PROYEK	
JL. TENTARA PELAJAR, GIRIWONO, WONOGIRI	
GAMBAR	SKALA
DETAIL PINTU	1 : 100
DIGAMBAR	
BAGGUS PRASTYO S.T	
DIPERIKSA	DISETUJUI
HALAMAN	JML. HALAMAN

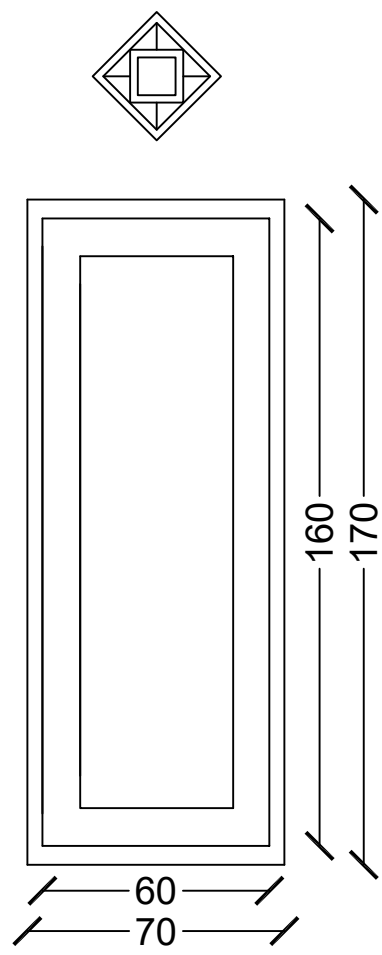

 **DETAIL J1**
SKALA 1 : 20

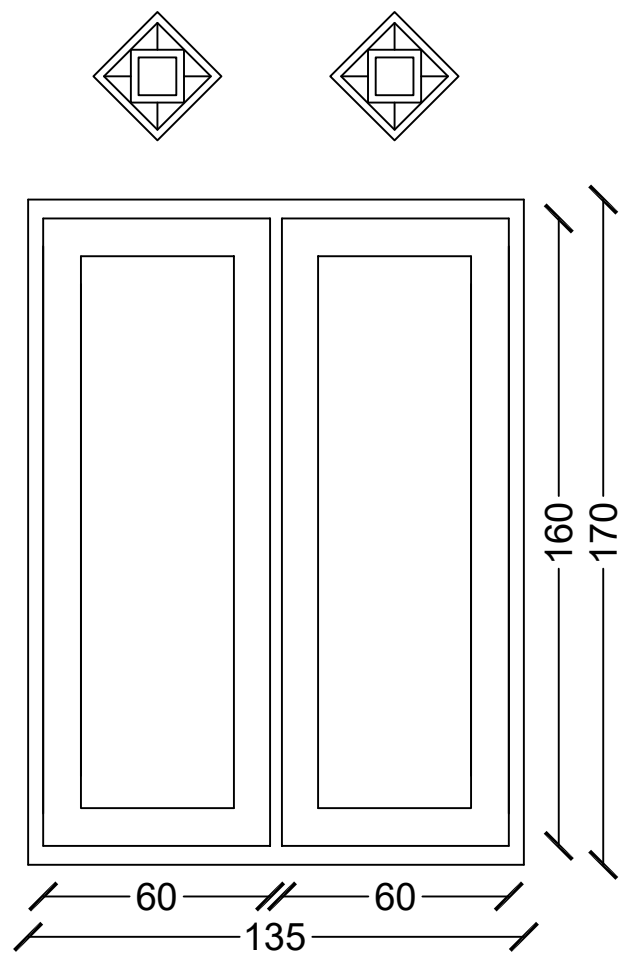


 **DETAIL J2**
SKALA 1 : 20

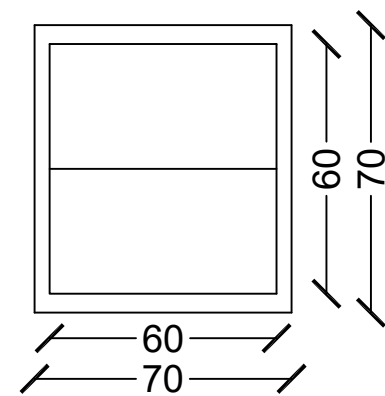

 **DETAIL BV**
SKALA 1 : 20


NAMA PROYEK	
PEMBANGUNAN RUKO KLINIK BERSALIN & BABY SPA 2 LANTAI	
ALAMAT PROYEK	
JL. TENTARA PELAJAR, GIRIWONO, WONOGIRI	
GAMBAR	SKALA
DETAIL PINTU	1 : 100
DIGAMBAR	
BAGGUS PRASTYO S.T	
DIPERIKSA	DISETUJUI
HALAMAN	JML. HALAMAN

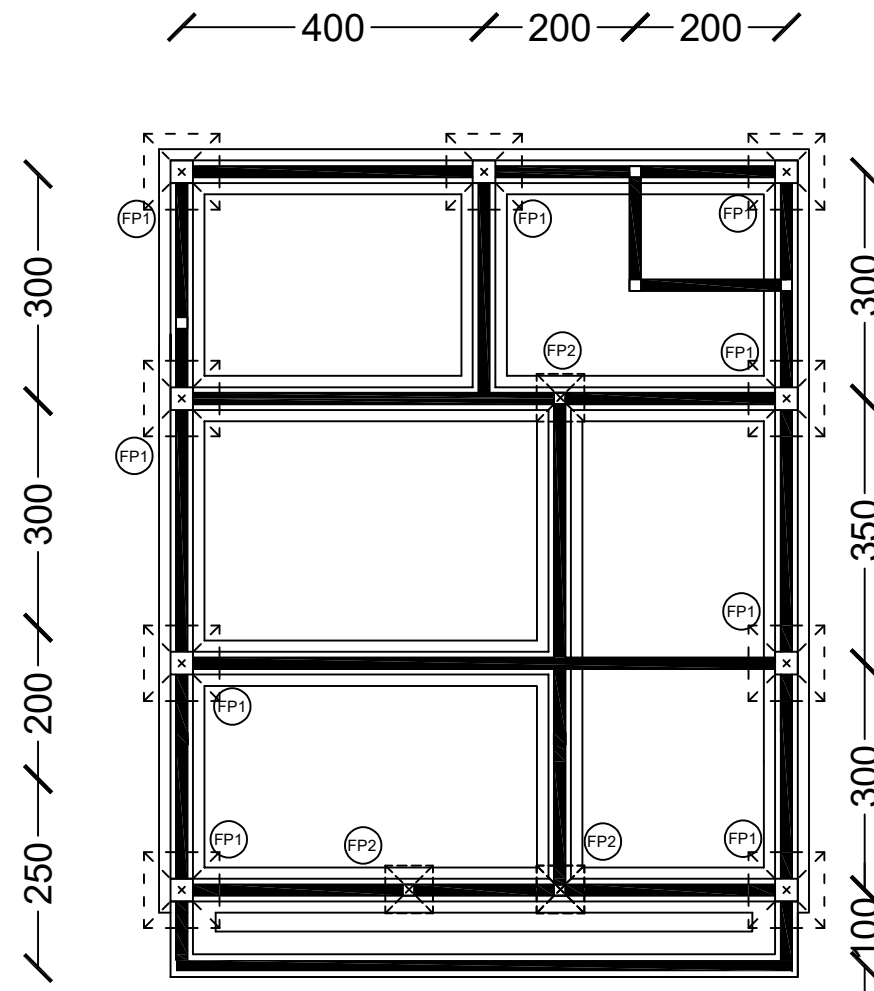


DENAH PONDASI

SKALA 1 : 100


PENULANGAN KOLOM STRUKTUR 30 X 30

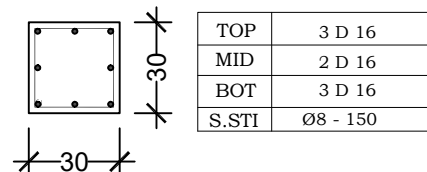


PENULANGAN KOLOM PRAKTIS 15 X 15

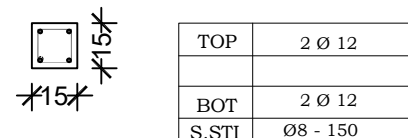


PENULANGAN SLOOF 15 X 25

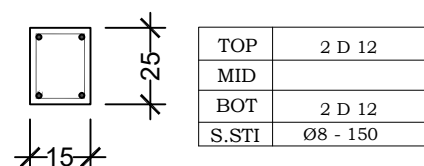

DETAIL PONDASI FOOTPLATE1 100x100

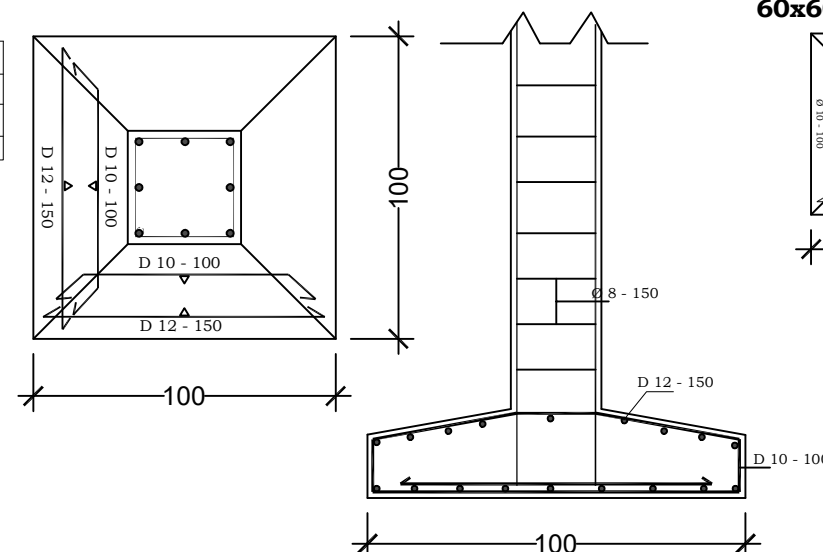

DETAIL PONDASI FOOTPLATE2 60x60

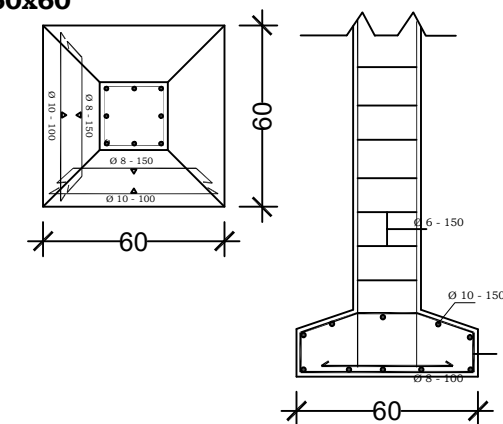

NAMA PROYEK

PEMBANGUNAN RUKO
KLINIK BERSALIN & BABY SPA
2 LANTAI

ALAMAT PROYEK

JL. TENTARA PELAJAR, GIRIWONO,
WONOGIRI

GAMBAR

SKALA

DENAH PONDASI

1 : 100

DIGAMBAR


BAGGUS PRASTYO S.T

DIPERIKSA

DISETUJUI


HALAMAN

JML. HALAMAN

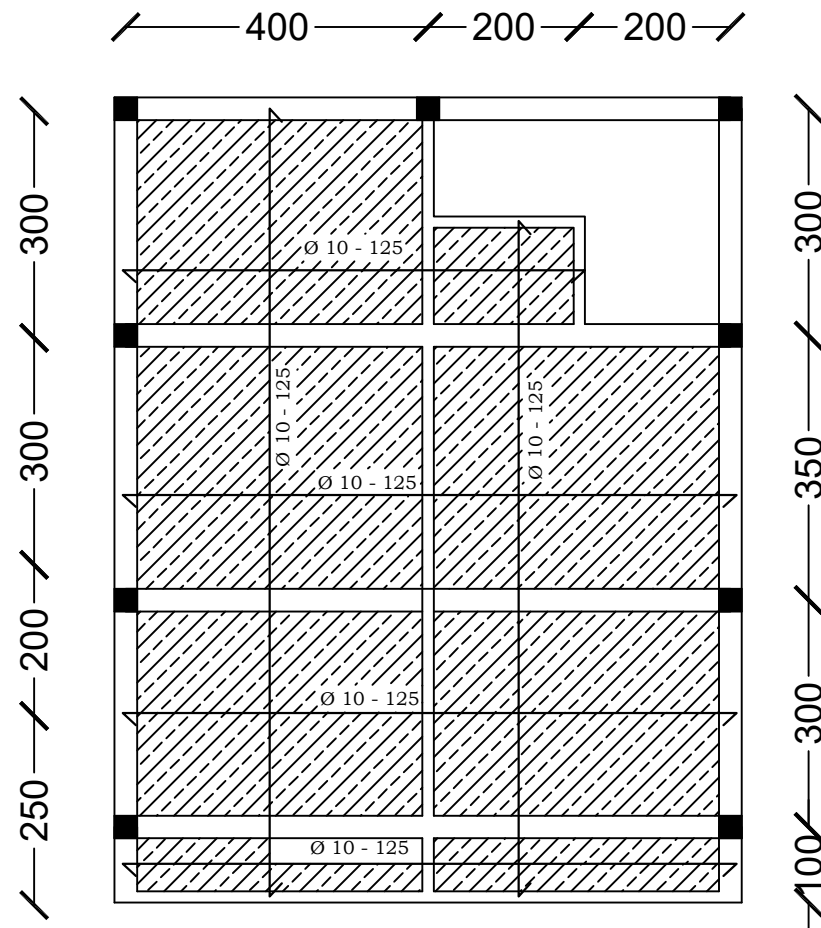


DENAH BETON LT2
SKALA 1 : 100

PENULANGAN BALOK INDUK 30 X 60

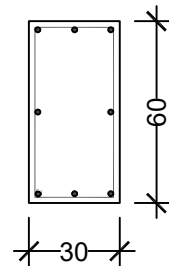


TOP	3 D 16
MID	2 D 16
BOT	3 D 16
S.STI	Ø8 - 150

PENULANGAN TALANG BETON

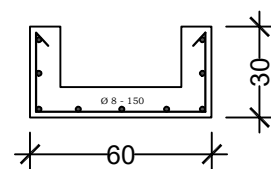

**PENULANGAN BALOK ANAK & RING
15 X 25**

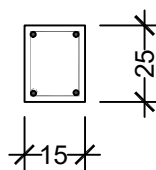

TOP	2 D 12
MID	
BOT	2 D 12
S.STI	Ø8 - 150

NAMA PROYEK

PEMBANGUNAN RUKO
KLINIK BERSALIN & BABY SPA
2 LANTAI

ALAMAT PROYEK

JL. TENTARA PELAJAR, GIRIWONO,
WONOGIRI

GAMBAR

SKALA

DENAH BETON

1 : 100

DIGAMBAR


BAGGUS PRASTYO S.T

DIPERIKSA

DISETUJUI


HALAMAN

JML. HALAMAN

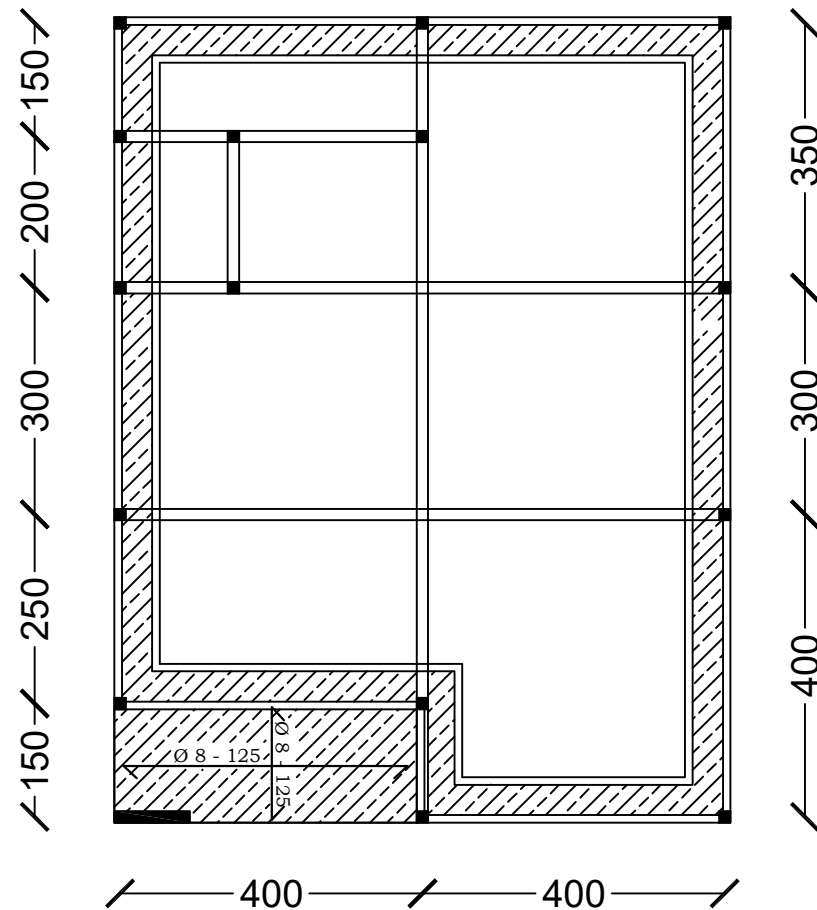


DENAH RING LT2
SKALA 1 : 100

PENULANGAN RING 15 X 20

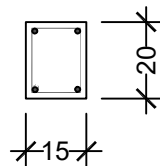

TOP	2 D 12
MID	
BOT	2 D 12
S.STI	Ø 8 - 150

PENULANGAN TALANG BETON

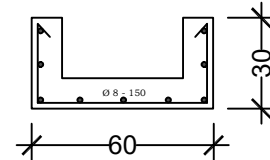

NAMA PROYEK

PEMBANGUNAN RUKO
KLINIK BERSALIN & BABY SPA
2 LANTAI

ALAMAT PROYEK

JL. TENTARA PELAJAR, GIRIWONO,
WONOGIRI

GAMBAR

SKALA

DENAH RING

1 : 100

DIGAMBAR


BAGGUS PRASTYO S.T

DIPERIKSA

DISETUJUI

HALAMAN

JML. HALAMAN

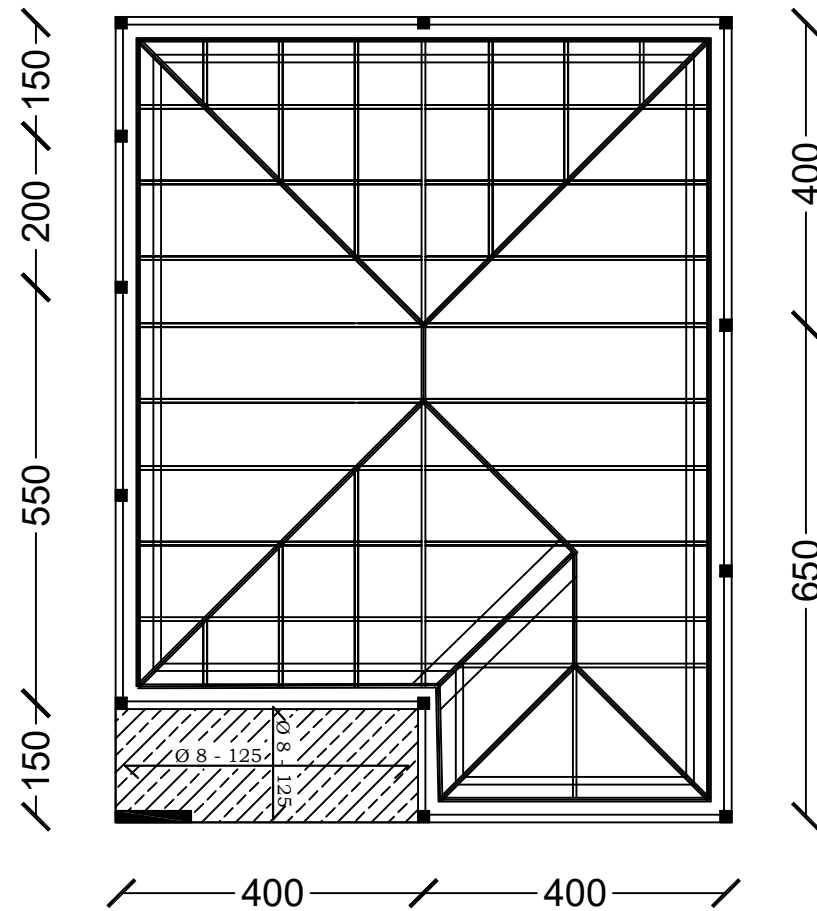

DENAH ATAP LT2
SKALA 1 : 100

TABEL ATAP

NO	KETERANGAN
1	RANGKA ATAP BAJA RINGAN & BETON
2	PENUTUP ATAP GENTENG
3	LISPLANK GRC 20 CM

NAMA PROYEK

PEMBANGUNAN RUKO
KLINIK BERSALIN & BABY SPA
2 LANTAI

ALAMAT PROYEK

JL. TENTARA PELAJAR, GIRIWONO,
WONOGIRI

GAMBAR

SKALA

DENAH ATAP

1 : 100

DIGAMBAR


BAGGUS PRASTYO S.T

DIPERIKSA


DISETUJUI

HALAMAN

JML. HALAMAN

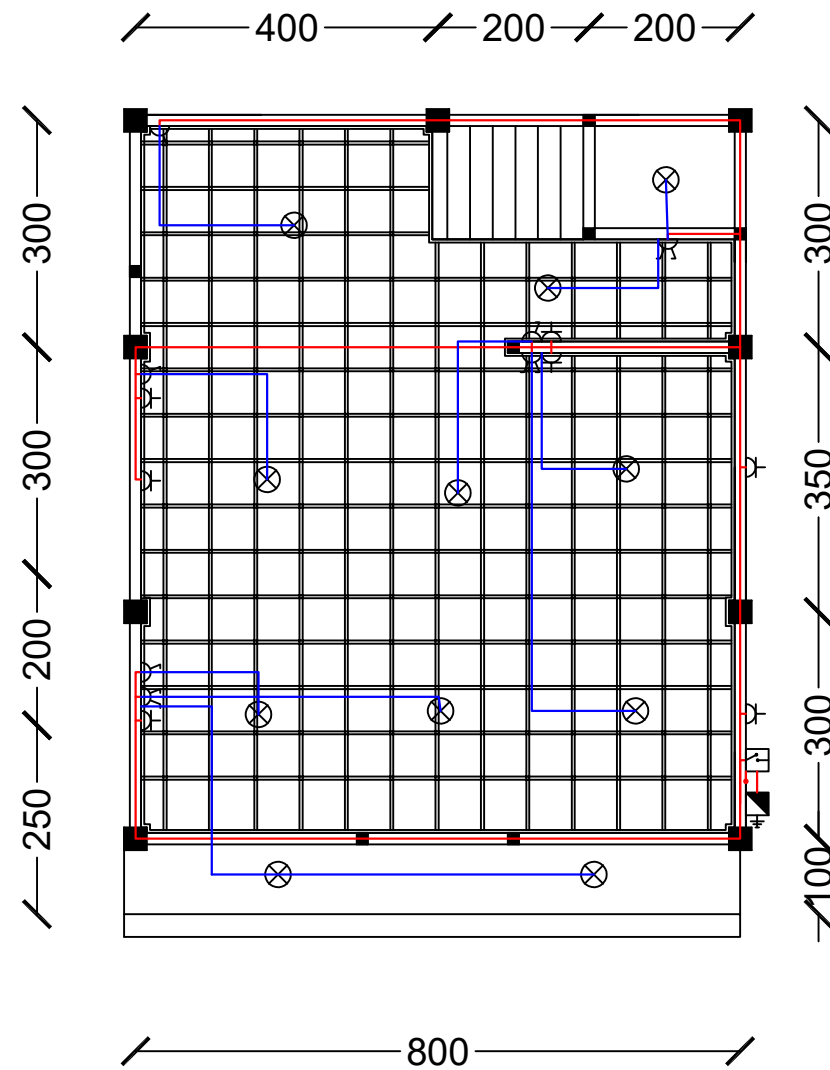

PLAFON & KELISTRIKAN LT 1
SKALA 1 : 100

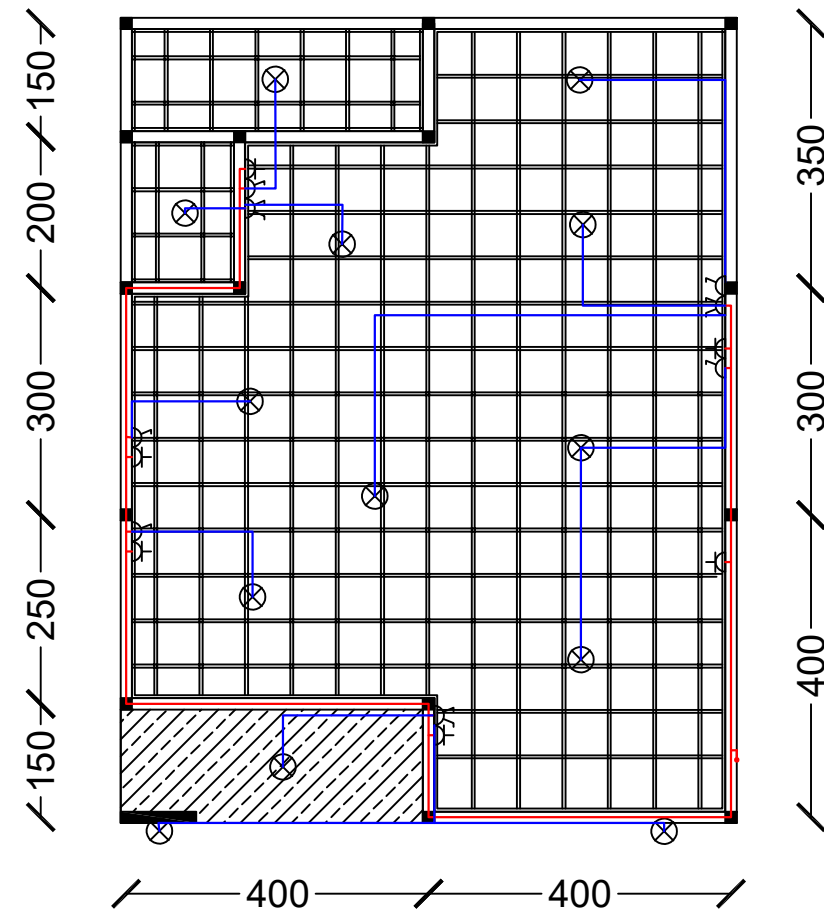

PLAFON & KELISTRIKAN LT 2
SKALA 1 : 100

TABEL INSTALASI AIR DAN SANITASI

KODE	KETERANGAN	JUMLAH
⊗	LAMPU	13
⌋	SAKLAR TUNGGAL	4
⌋⌋	SAKLAR GANDA	3
⌋⌋⌋	STOP KONTAK	6
⌋⌋⌋⌋	BOX MCB	
⌋⌋⌋⌋⌋	KWH	
—	KABEL LISTRIK	
—	KABEL LAMPU	
↓	TERHUBUNG LT 1-2	

NAMA PROYEK

PEMBANGUNAN RUKO
KLINIK BERSALIN & BABY SPA
2 LANTAI

ALAMAT PROYEK

JL. TENTARA PELAJAR, GIRIWONO,
WONOGIRI

GAMBAR

SKALA

DENAH PLAFON

1 : 100

DIGAMBAR


BAGGUS PRASTYO S.T

DIPERIKSA

DISETUJUI

HALAMAN

JML. HALAMAN

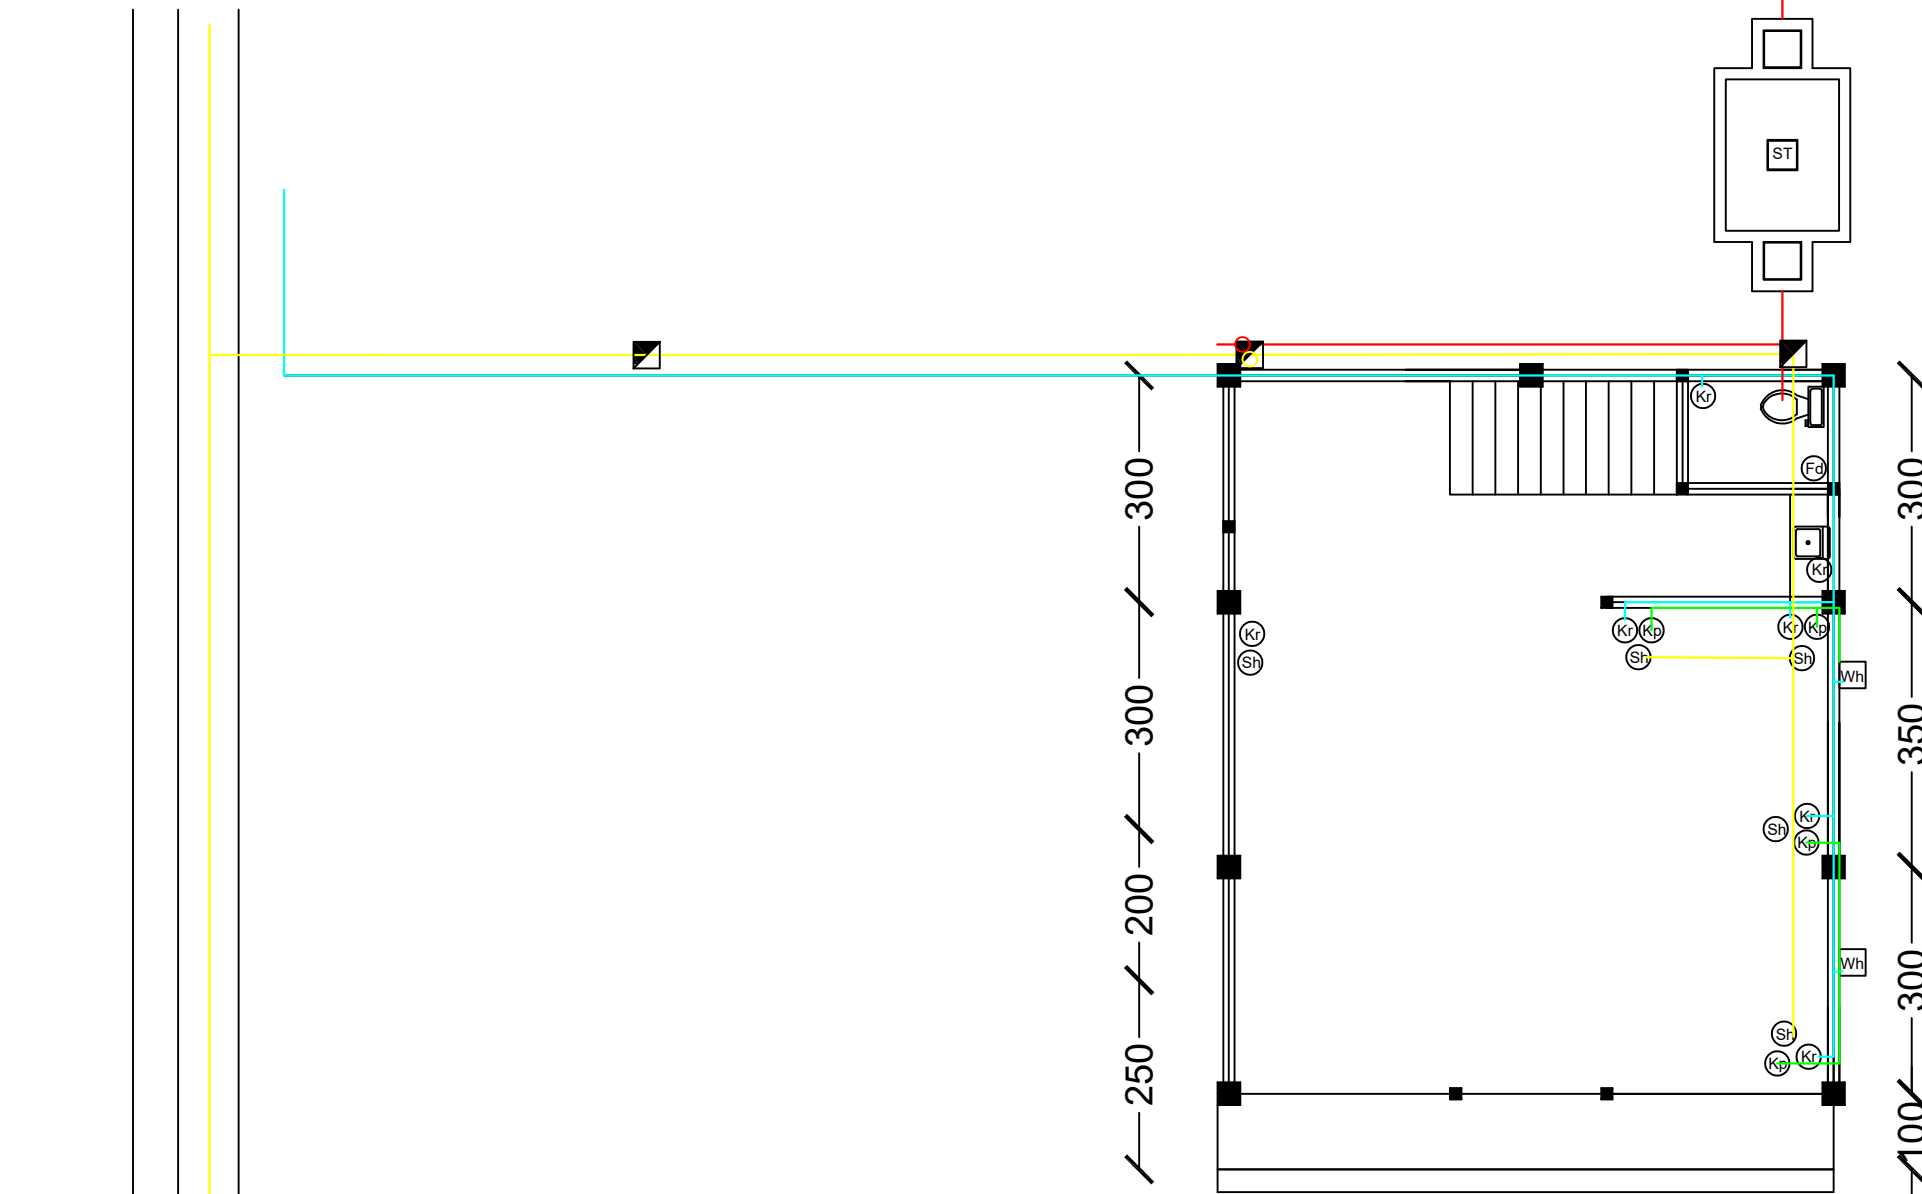

TABEL INSTALASI AIR DAN SANITASI

KODE	KETERANGAN	KODE	KETERANGAN
Kr	KRAN AIR	—	PIPA AIR BERSIH 3/4"
Kp	KRAN AIR PANAS	—	PIPA AIR PANAS 3/4"
Klo	KLOSET	—	PIPA DRAINASE 3"
Fd	FLOOR DRAIN	—	PIPA SANITASI 4"
Wb	WASH BAK	■	BAK CONTROL
Sh	SINK HOLE	ST	SEPTIC TANK
Wh	WATER HEATER	R	RESAPAN

DENAH INSTALASI AIR DAN SANITASI LT 1
SKALA 1 : 100

NAMA PROYEK

PEMBANGUNAN RUKO
KLINIK BERSALIN & BABY SPA
2 LANTAI

ALAMAT PROYEK

JL. TENTARA PELAJAR, GIRIWONO,
WONOGIRI

GAMBAR

SKALA

DENAH SANITASI

1 : 100

DIGAMBAR


BAGGUS PRASTYO S.T

DIPERIKSA

DISETUJUI

HALAMAN

JML. HALAMAN

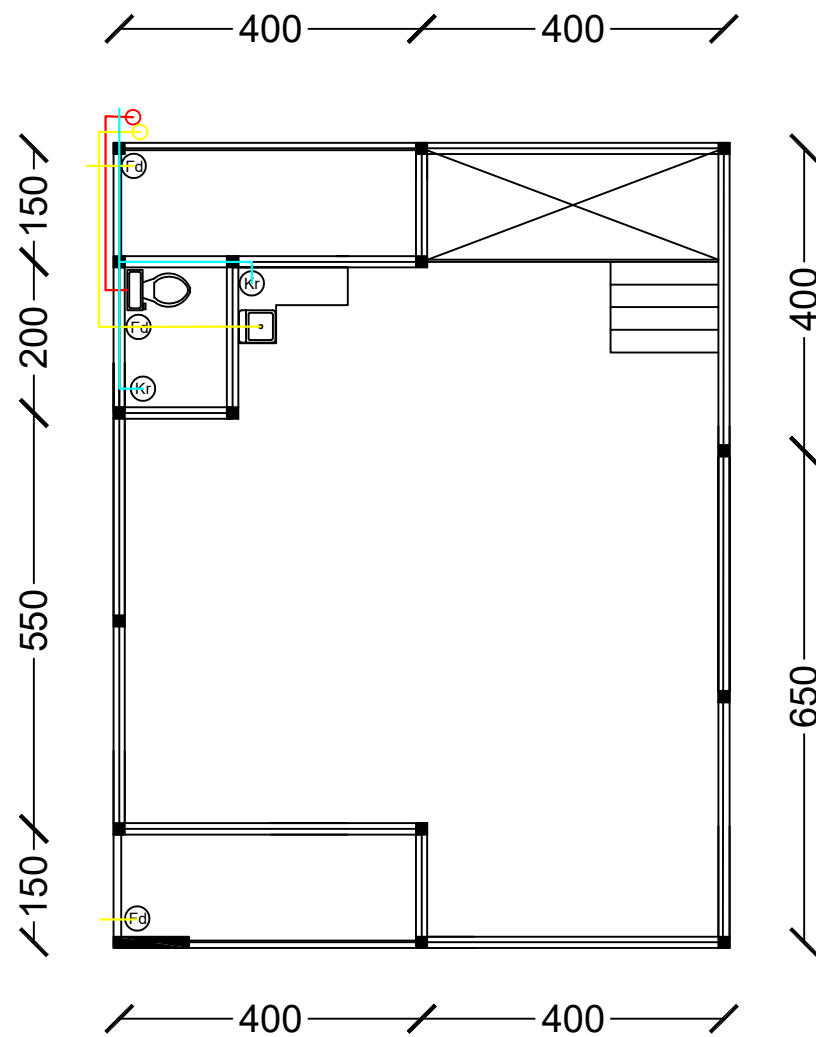

TABEL INSTALASI AIR DAN SANITASI

KODE	KETERANGAN	KODE	KETERANGAN
(Kr)	KRAN AIR	—	PIPA AIR BERSIH 3/4"
(Kp)	KRAN AIR PANAS	—	PIPA AIR PANAS 3/4"
(Toilet)	KLOSET	—	PIPA DRAINASE 3"
(Fd)	FLOOR DRAIN	—	PIPA SANITASI 4"
(Wb)	WASH BAK	■	BAK CONTROL
(Sh)	SINK HOLE	ST	SEPTIC TANK
(Wh)	WATER HEATER	R	RESAPAN

DENAH INSTALASI AIR DAN SANITASI LT 2

SKALA 1 : 100

NAMA PROYEK	
PEMBANGUNAN RUKO KLINIK BERSALIN & BABY SPA 2 LANTAI	
ALAMAT PROYEK	
JL. TENTARA PELAJAR, GIRIWONO, WONOGIRI	
GAMBAR	SKALA
DENAH LANTAI 1	1 : 100
DIGAMBAR	
BAGGUS PRASTYO S.T	
DIPERIKSA	DISETUJUI
HALAMAN	JML. HALAMAN